





Согласовано

Взам. инв. N

Подпись и дата

Инв. N подл.

Ситуационный план трассы переустройства
газопровода-отвода на ПК1868

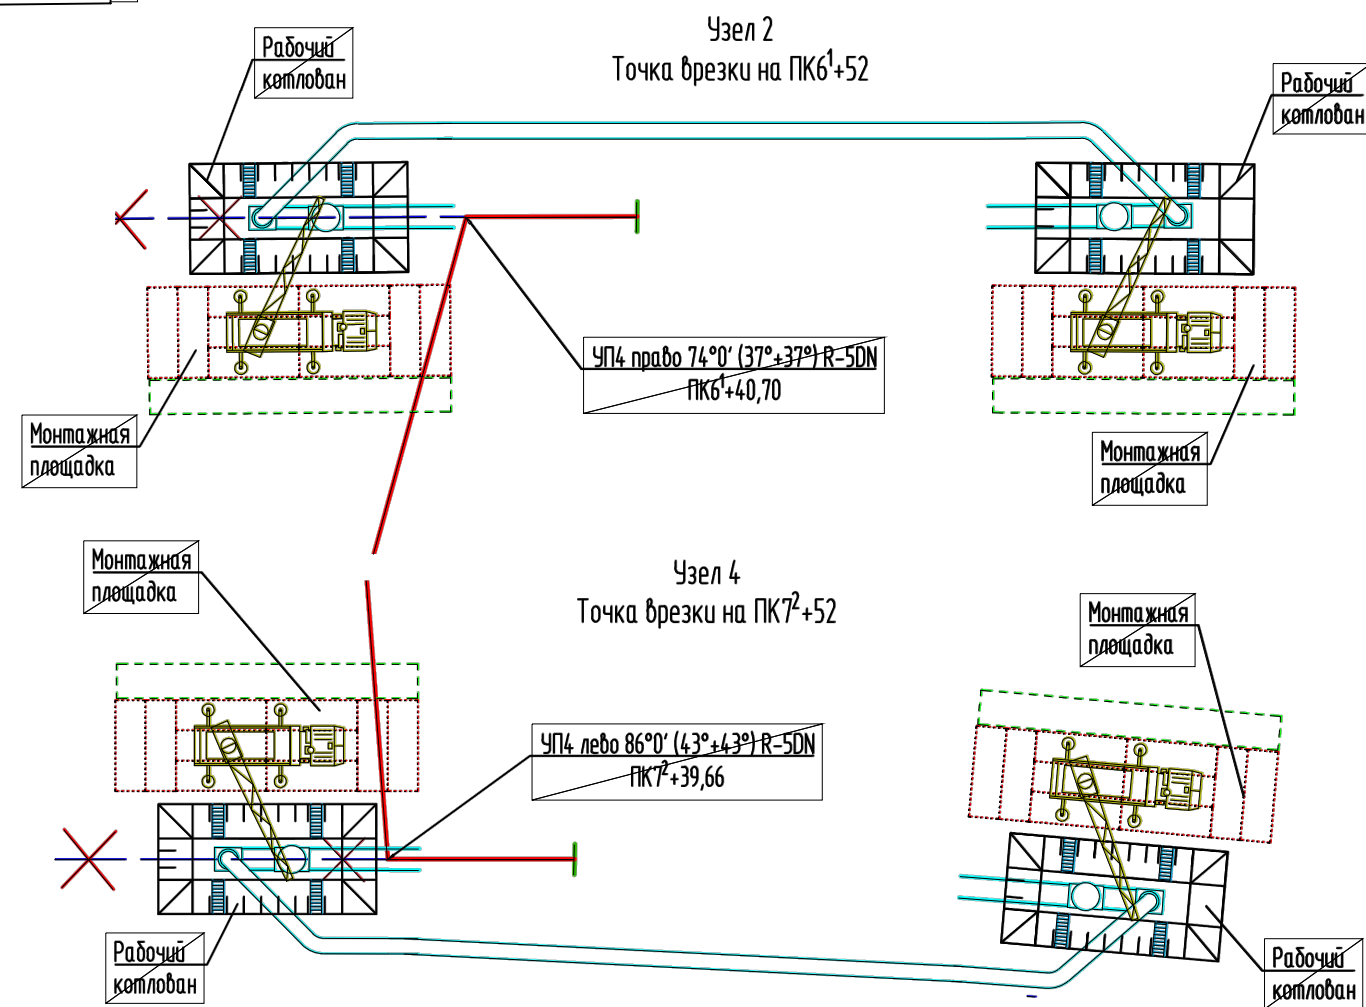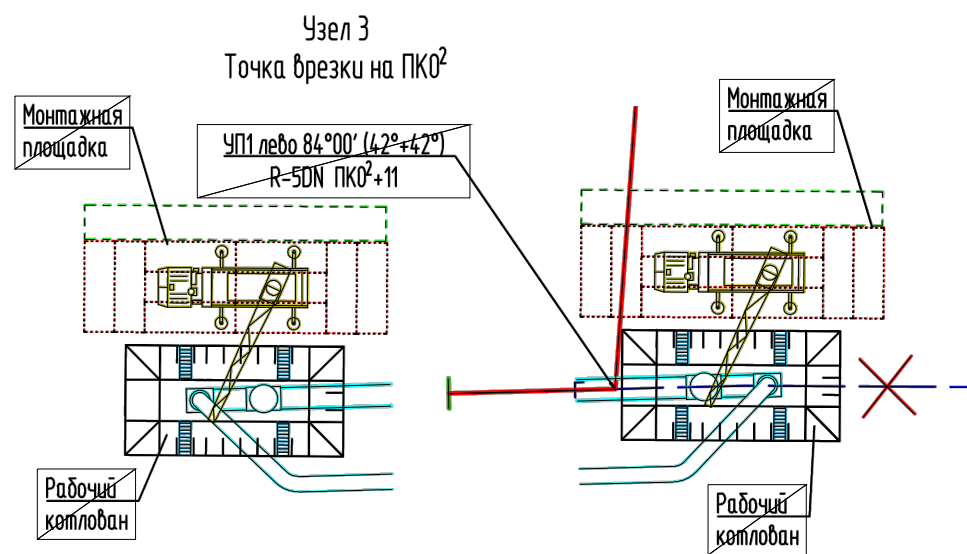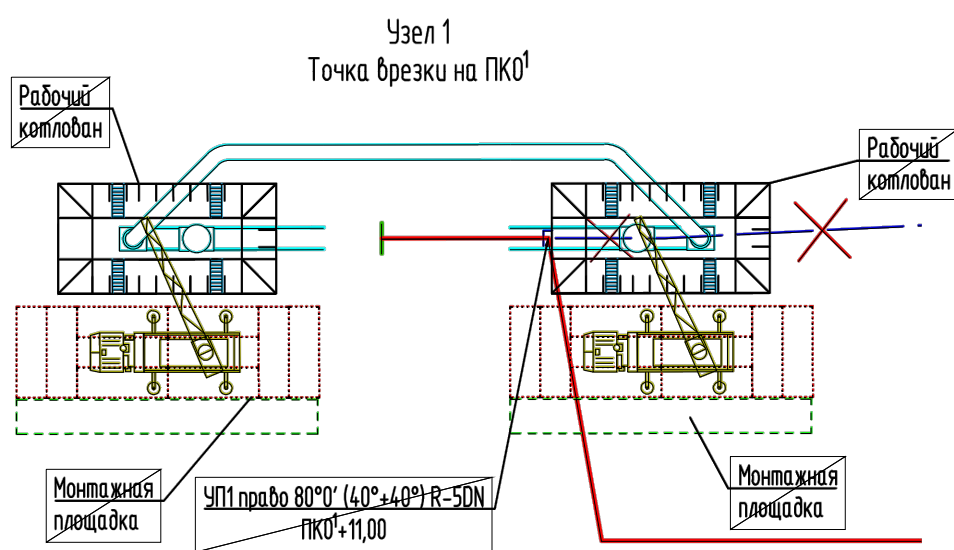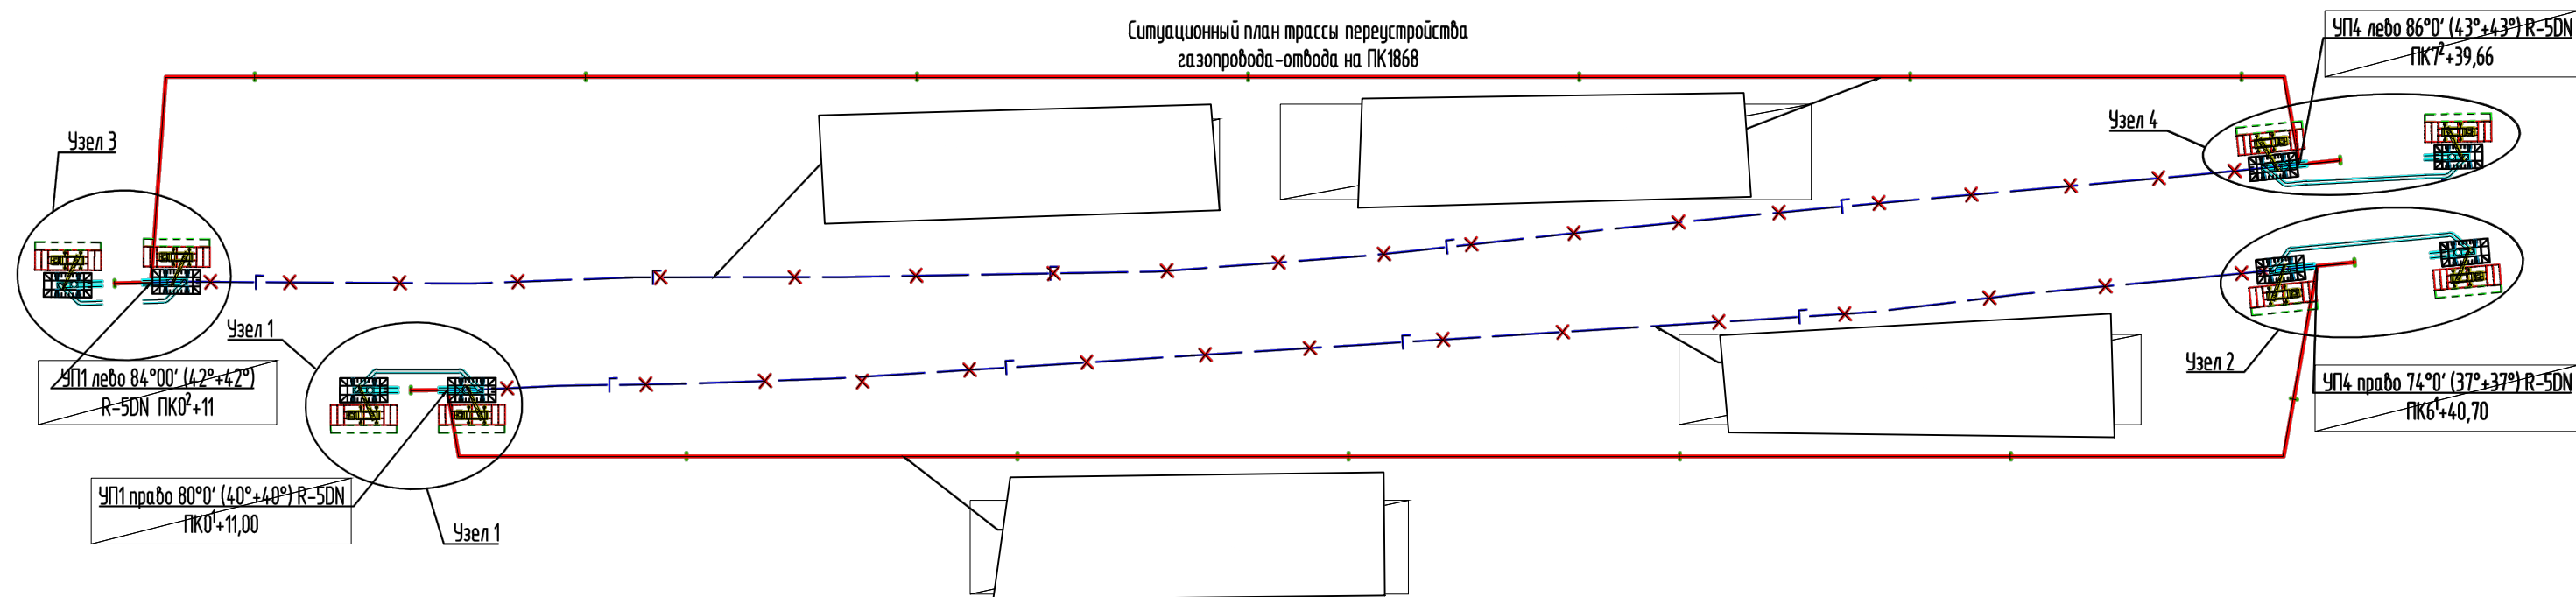

Условные обозначения

- Проектируемый участок газопровода высокого давления
- × — Демонтируемый участок газопровода