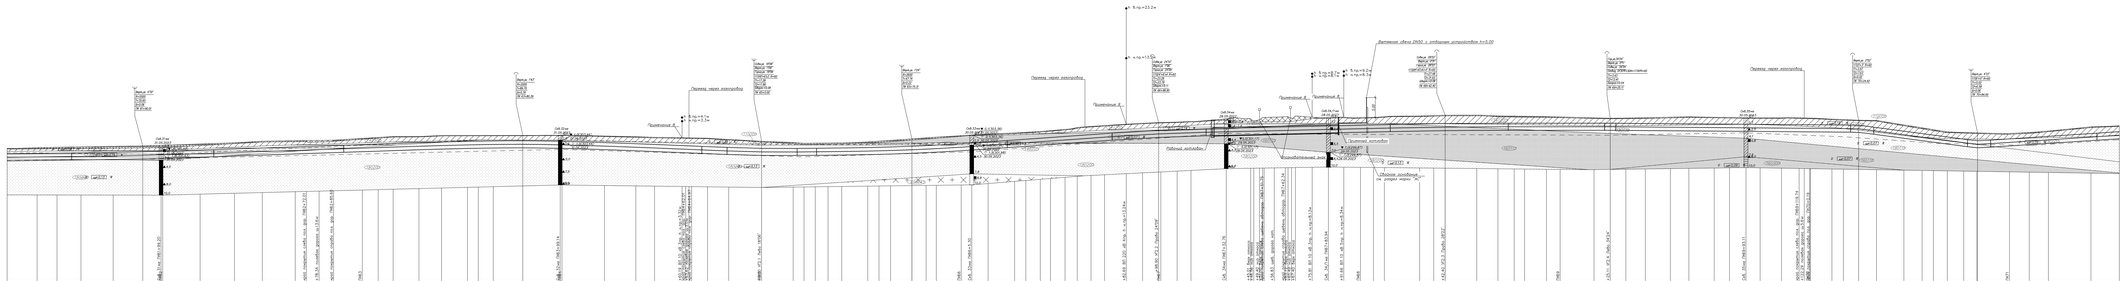

Ведомость кривых искусственного гнутья

Местоположение вершины угла		Плоскость поворота	Величина угла поворота		Радиус гибки гнутого отвода R, м / Ед. Ду	Количество типоразмеров отводов	Труба
КМ	ПК		град	мин			
6	65+0.00	Совм.	18	08	60.00	6°x3	1420x21.6
6	66+98.90	Совм.	24	10	60.00	6°x4	1420x25.8
6	68+42.40	Совм.	28	22	60.00	6°x4+4°	1420x21.6
6	69+25.11	Совм.	34	24	5Ду+60.00	30°+4°	1420x21.6
6	70+24.42	Верт.	2	52	60.00	3°	1420x21.6
7	70+84.00	Верт.	4	33	60.00	5°	1420x21.6

ГОРИЗОНТАЛЬНЫЙ 1:500
МАСШТАБЫ ВЕРТИКАЛЬНЫЙ 1:200
ГЕОЛОГИЧЕСКИЙ 1:200
275,00
Верт.уг. 0°30' R=5500 T=35.60 Б=0.06 ПК 61+90.01
Верт.уг. 1°43' R=2000 T=89.70 Б=0.34 ПК 63+80.39
Совм.уг. 18°08' Верт.уг. 1°09' Гориз.уг. 18°06' 1Г018°=6°x3 R=60 T1=17.28 T2=17.80 Бверт.=0.08 ПК 65+0.00
Верт.уг. 1°24' R=2600 T=47.74 Б=0.22 ПК 65+75.31
Совм.уг. 24°10' Верт.уг. 1°06' Гориз.уг. 24°09' 1Г024°=6°x4 R=60 T1=23.28 T2=23.79 Бверт.=0.11 ПК 66+98.90
Совм.уг. 28°22' Верт.уг. 0°31' Гориз.уг. 28°22' 1Г028°=6°x4+4° R=60 T1=27.48 T2=31.62 Бверт.=0.06 ПК 68+42.40
Гор.уг.34°24' Верт.уг. 0°11' Совм.уг. 34°24' Отвод 0°30'R=5DN+1Г04°R=60 T1=3.43 T2=13.41 Бгориз.=0.54 ПК 69+25.11
Верт.уг. 2°52' 1Г03°=3° R=60 T1=3.97 T2=7.63 Б=0.02 ПК 70+24.42
Верт.уг. 4°33' 1Г05°=5° R=60 T1=5.02 T2=6.58 Б=0.06 ПК 70+84.00
Переезд через газопровод
Примечание 8
Примечание 9
h в.пр.=4.1м h н.пр.=3.3м
h в.пр.=23.2м h н.пр.=13.2м
h в.пр.=8.7м h н.пр.=8.1м
h в.пр.=9.2м h н.пр.=8.3м
Вытяжная свеча DN50 с отборным устройством h=5.00
Рабочий котлован
Приемный котлован
Опознавательный знак
Свайное основание см. раздел марки "АС"
Скв.31мг 31.05.2023
Скв.32мг 31.05.2023
Скв.33мг 30.05.2023
Скв.34мг 28.05.2023
Скв.34/1мг 28.05.2023
Скв.35мг 30.05.2023
Скв. 31мг ПК61+99.20
край покрытия слева пол. дор. ПК62+72.01
+78.34 полевая дорога ш.13.6м
край покрытия справа пол. дор. ПК62+85.60
Скв. 32мг ПК63+99.14
+60.19 ВЛ 10 кВ 3пр. h н.пр.=3.32м
край покрытия слева пол. дор. ПК64+62.01
+63.62 полевая дорога ш.3.0м
край покрытия справа пол. дор. ПК64+64.97
+0.00 УГ2.1 Лево 18°06'
Скв. 33мг ПК66+5.30
+82.69 ВЛ 220 кВ 4пр. h н.пр.=13.24м
+98.90 УГ2.2 Право 24°09'
Скв. 34мг ПК67+32.76
край покрытия слева щебень автодор. ПК67+51.75
+56.83 щеб. дорога кат.
край покрытия справа щебень автодор. ПК67+62.34
+75.81 ВЛ 10 кВ 3пр. h н.пр.=8.13м
Скв. 34/1мг ПК67+83.94
+91.66 ВЛ 10 кВ 5пр. h н.пр.=8.34м
+42.40 УГ2.3 Право 28°22'
+25.11 УГ2.4 Лево 34°24'
Скв. 35мг ПК69+93.11
край покрытия слева пол. дор. ПК69+119.74
+122.29 полевая дорога ш.5.6м
край покрытия справа пол. дор. ПК70+0.19
Инженерно-геологическая характеристика
Амуро-Зейская равнина. Островное распространение ММГ. Мерзлота сливающегося типа.
Удельное электросопротивление грунта, Ом м
150–300
50–100
500–1000
Угодья
лес
неудобные земли
вырубка
луг
Пикетаж
Расстояние между отметками, м
Отметка земли, м
Планировочные отметки, м
Откосы траншеи / Ширина дна траншеи, м
1:1.25 / 3.10
1:0.75 / 2.10
1:0.75 / 2.60
Проектные отметки (верх трубы), м
Уклон газопровода
Длина участка, м
Тип прокладки
Тип 3, L=535.90
ГНБ, L=65,00
Тип 1, L=522.00
Глубина траншеи, м
Категория участка газопровода / Труба ФxS, мм
III / 1420x21.6 Рисп.=1.1Рраб.–пневматически
I / 1420x25.8 Предв. пневматическое испытание Рисп.=1.25Рраб. Пневматическое испытание Рисп.=1.1Рраб.
Тип изоляции газопровода
Заводское монослойное полиэтиленовое покрытие
Защита изоляции от механических повреждений
Кольца опорно-направляющие Ф1420–34шт., шаг 2.00
Балластировка и закрепление газопровода (тип балласта или крепежа, кол., шаг)
УБО-УМ-1420 13шт. с шагом 2.80м.
УБО-УМ-1420 29шт. с шагом 2.50м.
УБО-УМ-1420 23шт. с шагом 2.80м.
УБО-УМ-1420 67шт. с шагом 2.70м.
УБО-УМ-1420 21шт. с шагом 2.80м.
УБО-УМ-1420 40шт. с шагом 2.40м.
УБО-УМ-1420 13шт. с шагом 2.80м.
Защитный кожух ФxS, мм / длина, м
Кожух Ф1720x16, L=63.00
Нормативная глубина сезонного оттаивания и промерзания
2.7
2.8
3.4
2.9
3.0
Теплоизоляция
Защита трубопровода от механических повреждений
подушка S=0.20 обсыпка S=0.20
Взам. инв. N°
Подп. и дата
Инв. N° подл.
004836/0004

Изм.	Кол.уч.	Лист	N док.	Подп.	Дата		Стадия	Лист	Листов
Разраб.									
Пров.									
Гл.спец.									
Н.контр.									

Формат А2x6