



M1: 10

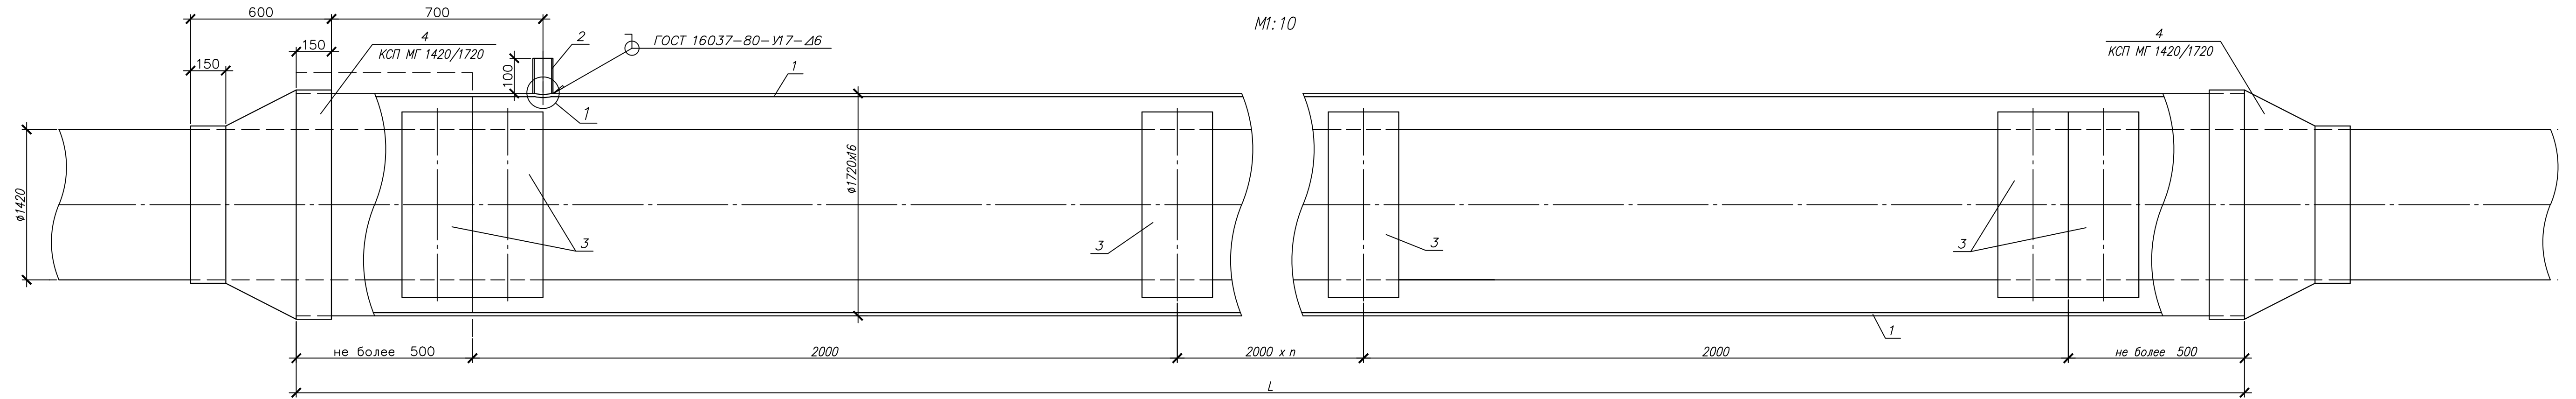

1. Количество предохранительных диэлектрических колец "Спейсеры" берется из расчета $(L-1)/2+3=n$, где L —длина защитного кожуха, n — количество предохранительных диэлектрических колец.
2. Устройство защиты манжет УЗМ-1420/1720 показано условно.

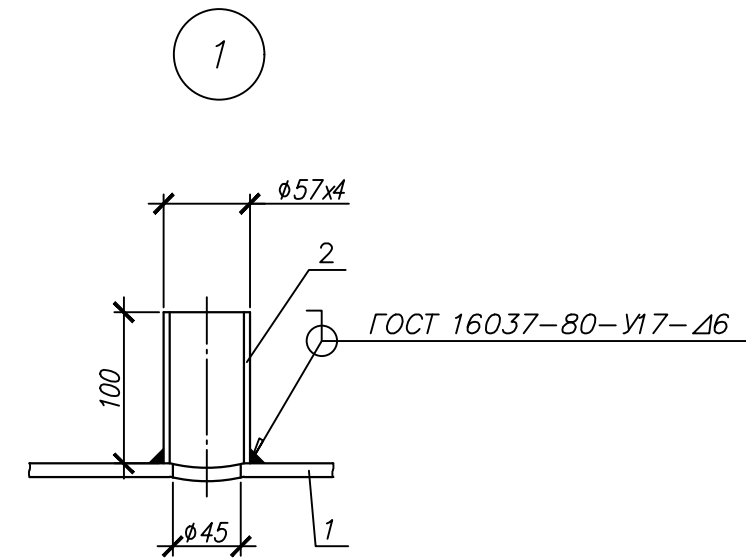

Спецификация (Кожух DN1700)

Поз	Обозначение	Наименование	Кол.	Масса ед, кг	Примечание
1	ТУ 1381-002-13152697-2015	Труба - 1720х16,0-3Ф-К60 (СМР открытым способом)	L	679.10	
2	ТУ 14-3Р-137-2015	Труба БШ С-57,0х4,0-К48-t60/60	0.10	5.63	
3	ТУ 2291-034-00203803-2011	Кольца предохранительные диэлектрические "Спейсеры" 1420-1-3	n		
4	ТУ 25.11.23-002-67319596-2019	Комплект для строительства переходов (КСП) манжета герметизирующая МГ 1020/1420	1	6,1	в 1 комплекте 2 манжеты с хомутами
5	ТУ 1381-002-13152697-2015	Труба - 1720х16,0-3Ф-К60-ПЭПк-1-С (ННБ)	L	696.70	

Изм.	Кол.уч.	Лист	№ док.	Подпись	Дата			
Разраб.						Стадия	Лист	Листов
Пров.								
Гл. спец.								
Н. контр.								

Инв. N° подл.	Подп. и дата	Взам. инв. N°
---------------	--------------	---------------