
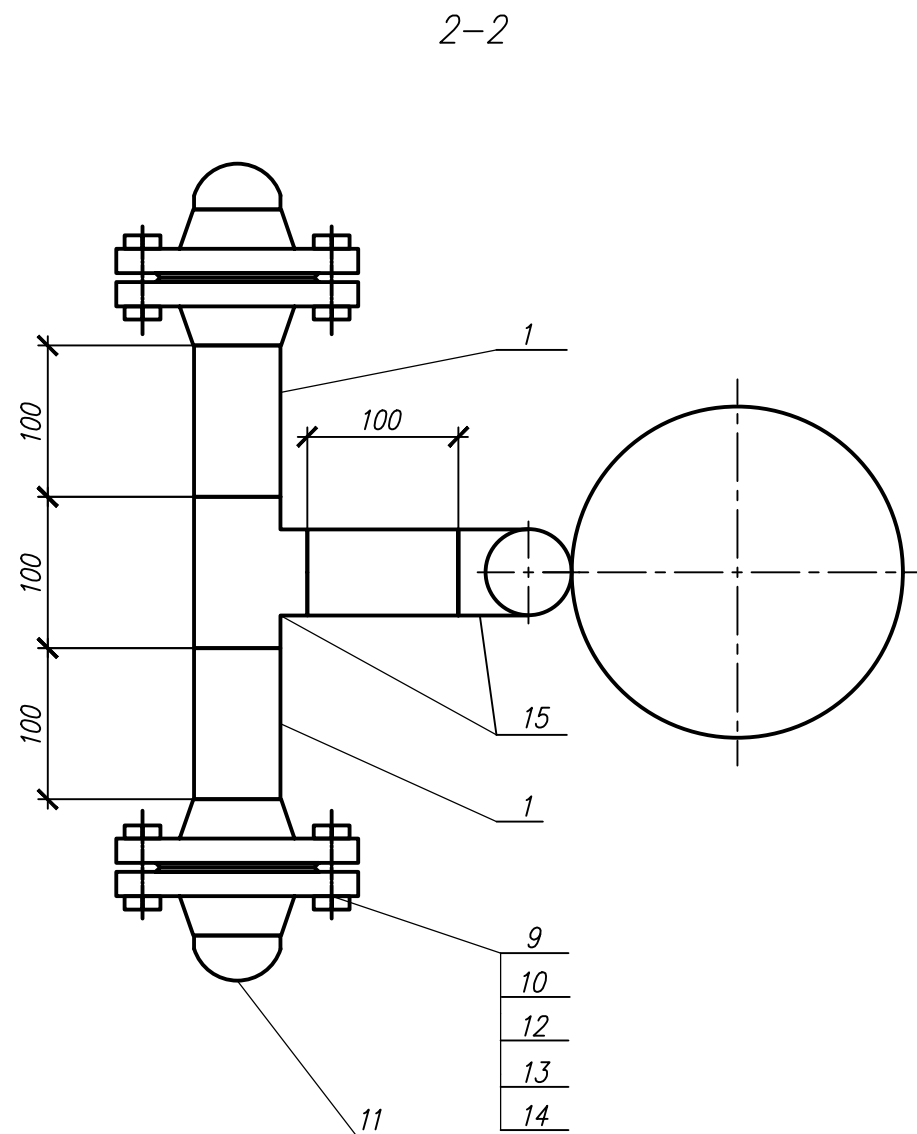
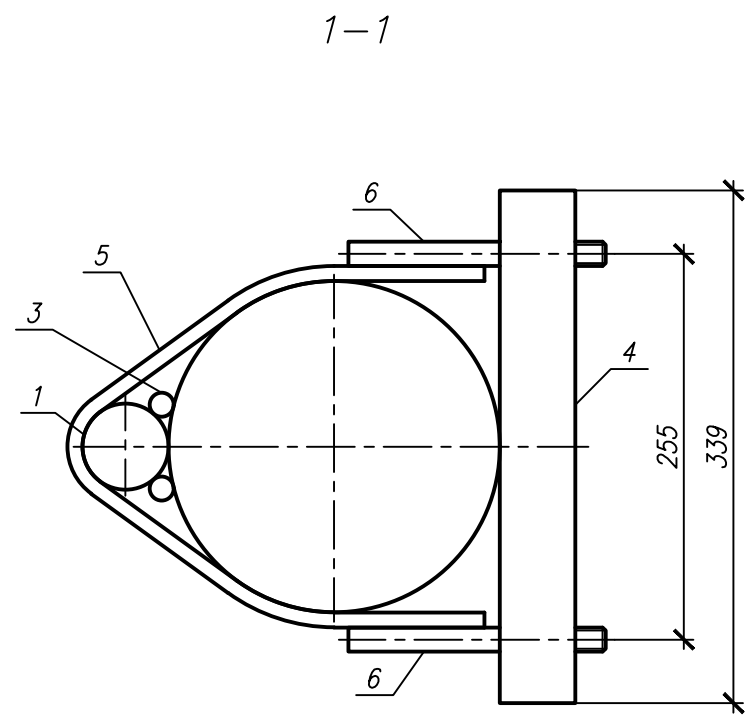
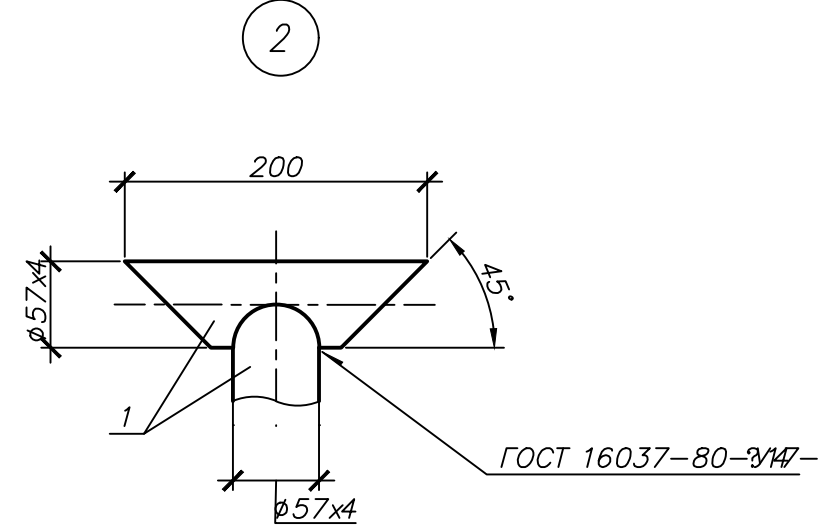
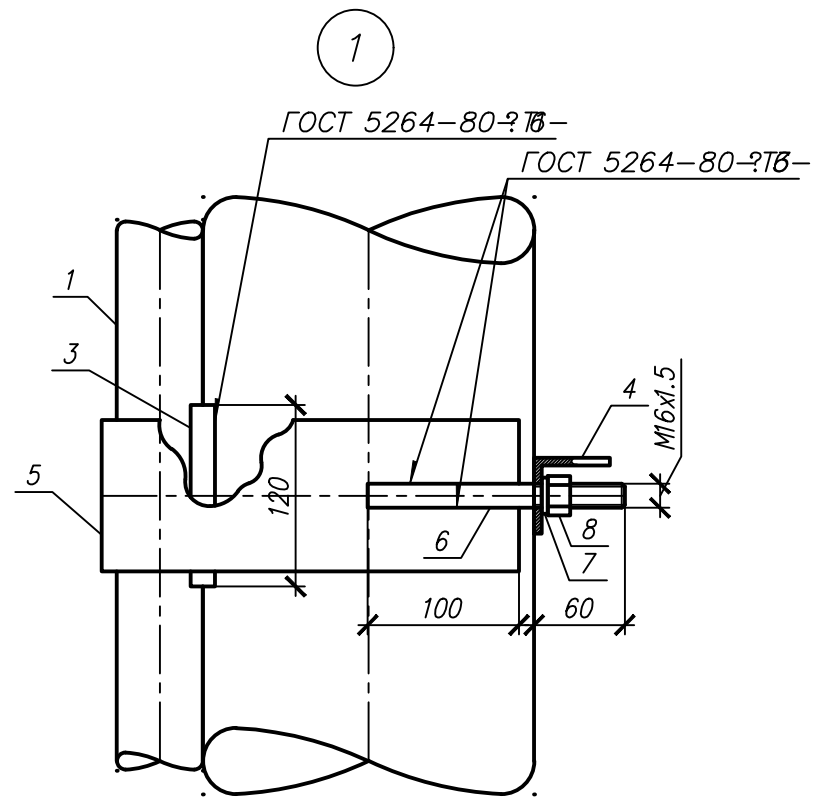



Схема свечи

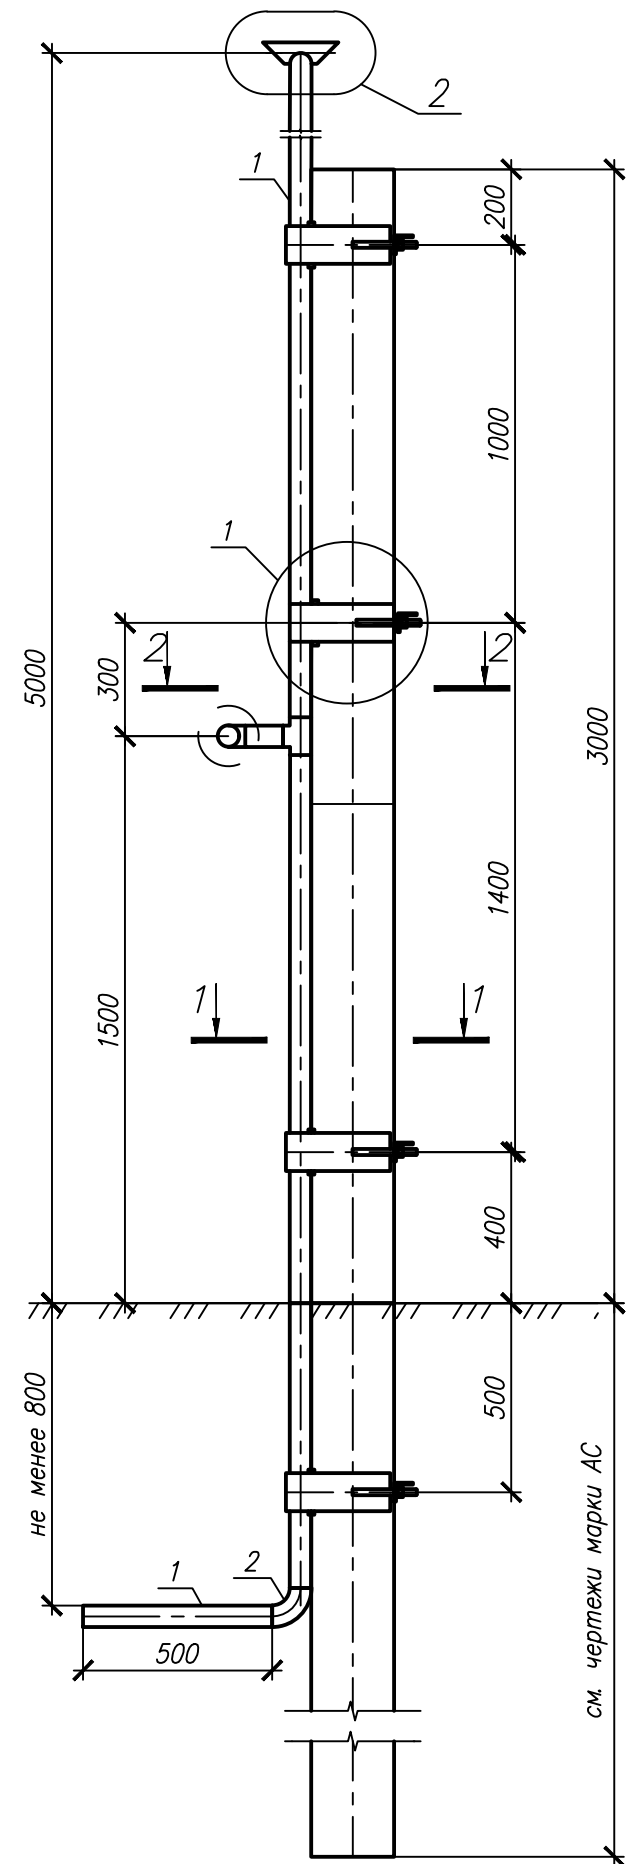

Спецификация					
Поз	Обозначение	Наименование	Кол.	Масса ед. кг	Примечание
1	ТУ 14-3Р-137-2015	Труба БШ-С-57х4-К48-Т60/60	20.0	5.23	
2	ТУ 1469-017-38948552-2015	Отвод ОК I 90°-57(4К48)	3	0.8	
3		Круг Б-16 ГОСТ 2590-2006 325-09Г2С ГОСТ 19281-2014	8	0.20	L=120
4		Уголок 50х5 ГОСТ 8509-93 345-09Г2С ГОСТ 19281-2014	4	1.28	L=339
5		Полоса 10х100-В-1 ГОСТ 103-2006 345-09Г2С ГОСТ 19281-2014	4	5.06	L=645
6		Круг Б-16 ГОСТ 2590-2006 325-09Г2С ГОСТ 19281-2014	8	0.27	L=170
7	ГОСТ 6402-70	Шайба 16 09Г2С	8	0.006	
8	ГОСТ ISO 4032-2014	Гайка шестигранная нормальная М16-6	8	0.038	
9	ГОСТ 33259-2015	Фланец 50-1-11-1-Е-Ст09Г2С-IV	2	1.26	
10	ГОСТ 33259-2015	Фланец 50-1-11-1-Ф-Ст09Г2С-IV	2	1.26	
11	ТУ 1469-017-38948552-2015	Днище Д I 57(4К48)-9.8(12.74)-С-20	2	0.22	
12	ГОСТ 9066-75	Шпилька АМ24-6х120.48.09Г2С.IV.2	8	0.371	
13	ГОСТ 9064-75	Гайка АМ24-6Н.09Г2С.IV.2	16	0.133	
14	ГОСТ 9065-75	Шайба 24.09Г2С.IV.2	16	0.009	
15	ТУ 1469-017-38948552-2015	Тройник Т I 57(4К48)-9.8(12.74)-0.825-60	2	0.9	

3 Трубы и соединительные детали изолируются системой антикоррозионного покрытия "Карбофлекс" (для подземной части) и эмалью «Унипол Б» по грунтовке «Унипол Б» (для надземной части).

Поз. 4

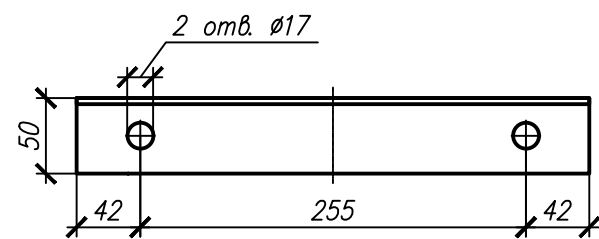[illegible]