
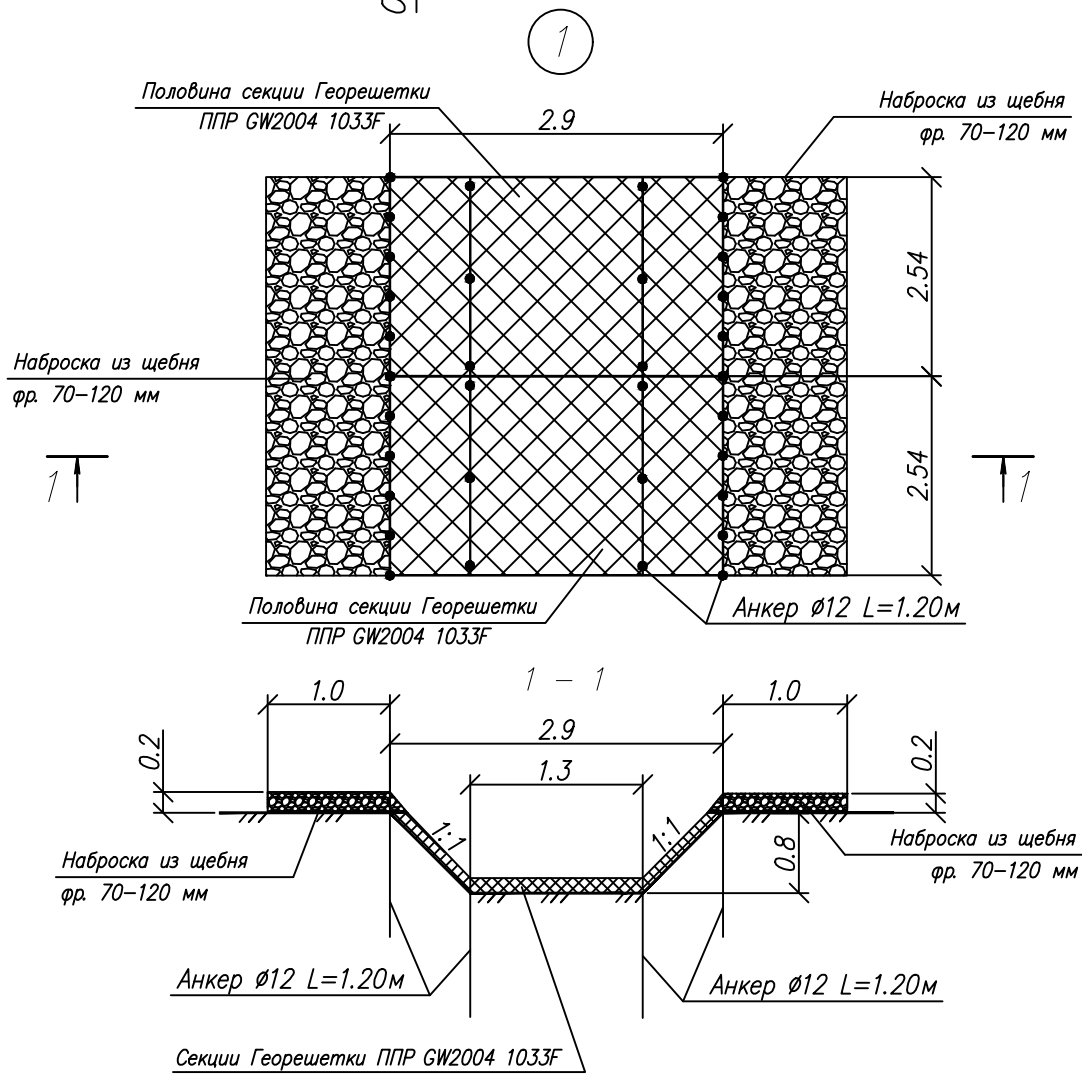


Схема поперечного профиля

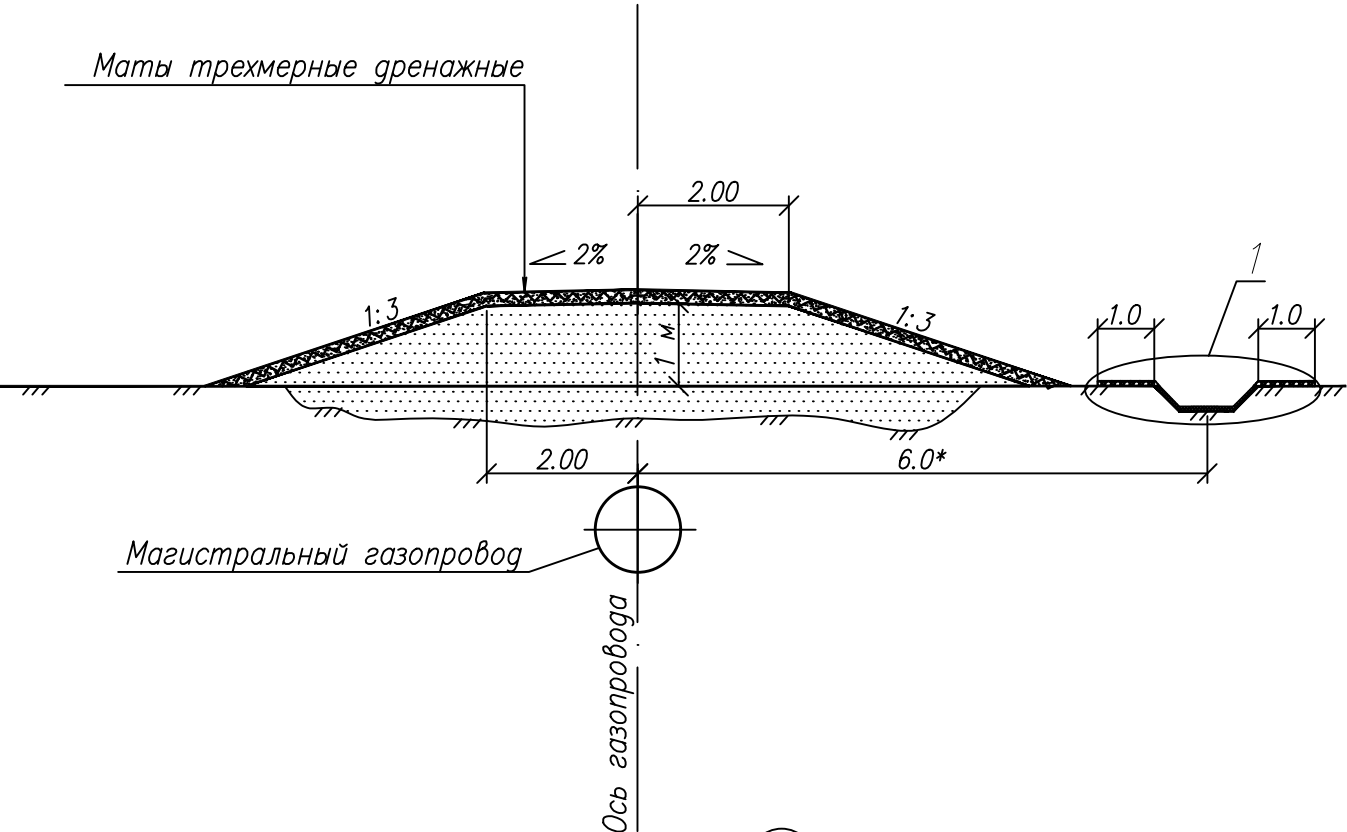

Объем работ на 100 п.м. укрепляемой канавы с заполнением ячеек щебнем

	Наименование работ	Ед. изм.	Количество	Примечание
1	Разработка с перемещением до 70 м бульдозерами мощностью 330 л.с. (группа грунта I)	м³	168	
2	Разравнивание лишнего грунта I группы бульдозером (мощн. 330 л.с.)	м³	168	
3	Разбивка планового положения секций Георешетки ППР GW2004 1033F с помощью шнуров и металлических штырей	шт	20	
4	Растягивание секций Георешеток ППР GW2004 1033F вручную до нормативной длины	м²	290	
5	Скрепление ребер секций Георешетки ППР металлическими скрепками с помощью пневмостеплера:	шт	20	
5.1	Секции Георешетки ППР GW2004 1033F – 27.44кг	шт	20	
5.2	Скрепки (вес одной скрепки 0.003кг)	шт	3015	
6	Крепление секций Георешетки ППР металлическими анкерами пальцами, арматура А-II, Ø12мм, средняя длина 1.20м	шт	640	1 анкер m=1.06кг
7	Заполнение ячеек Георешетки ППР щебнем фр. 20–40 мм толщиной 0.10м	м³	36	
8	Укрепление бровки канавы наброской щебнем фр. 70–120 мм толщиной 0.20м	м³	40	
9	Разработка в карьере щебня одноковшовым экскаватором емкостью ковша 1.00м³ с погрузкой в автосамосвалы и подвозкой:	м³	76	

Боковая канава устраивается с нагорной стороны относительно магистрального газопровода.

Изм.	Кол.уч.	Лист	№ док.	Подпись	Дата			
Разраб.								
Пров.						Стадия	Лист	Листов
Гл. спец.								
Н. контр.								